


## GENERAL NOTES

- ALL DIMENSION ARE IN MILLIMETERS.
- THIS DRAWING IS THE PROPERTY OF A & M DESIGN STUDIO, IS NOT TO BE PRODUCED, COPIED HANDED OVER TO THIRD PARTY OR USED FOR ANY OTHER PURPOSE OTHER THEN FOR WHICH IT IS INTENDED.
- ALL DIMENSION SHALL BE VERIFIED ON SITE PRIOR TO START OF WORK, ANY DISCREPANCY SHALL BE BROUGHT TO THE NOTICE OF THE ARCHITECTS.
- THE CONTRACTOR MUST CHECK ALL DIMENSIONS AND DETAILS AND BE RESPONSIBLE FOR THE SAME, ANY DISCREPANCY SHALL BE BROUGHT TO THE NOTICE OF THE ARCHITECTS BEFORE EXECUTION.
- THIS DRAWING IS TO BE READ AND NOT MEASURED.
- THIS DRAWING SHOULD BE READ IN CONJUNCTION WITH RELEVANT WORKING AND DETAILED DRAWINGS.
- ALL MENTIONED HEIGHTS ARE WITH RESPECT TO INTERNAL FINISH FLOOR LEVEL FOR
- ALL STRUCTURAL DETAILS FOLLOW THE STRUCTURAL DRAWINGS WITH STRUCTURAL NOTIFICATIONS.

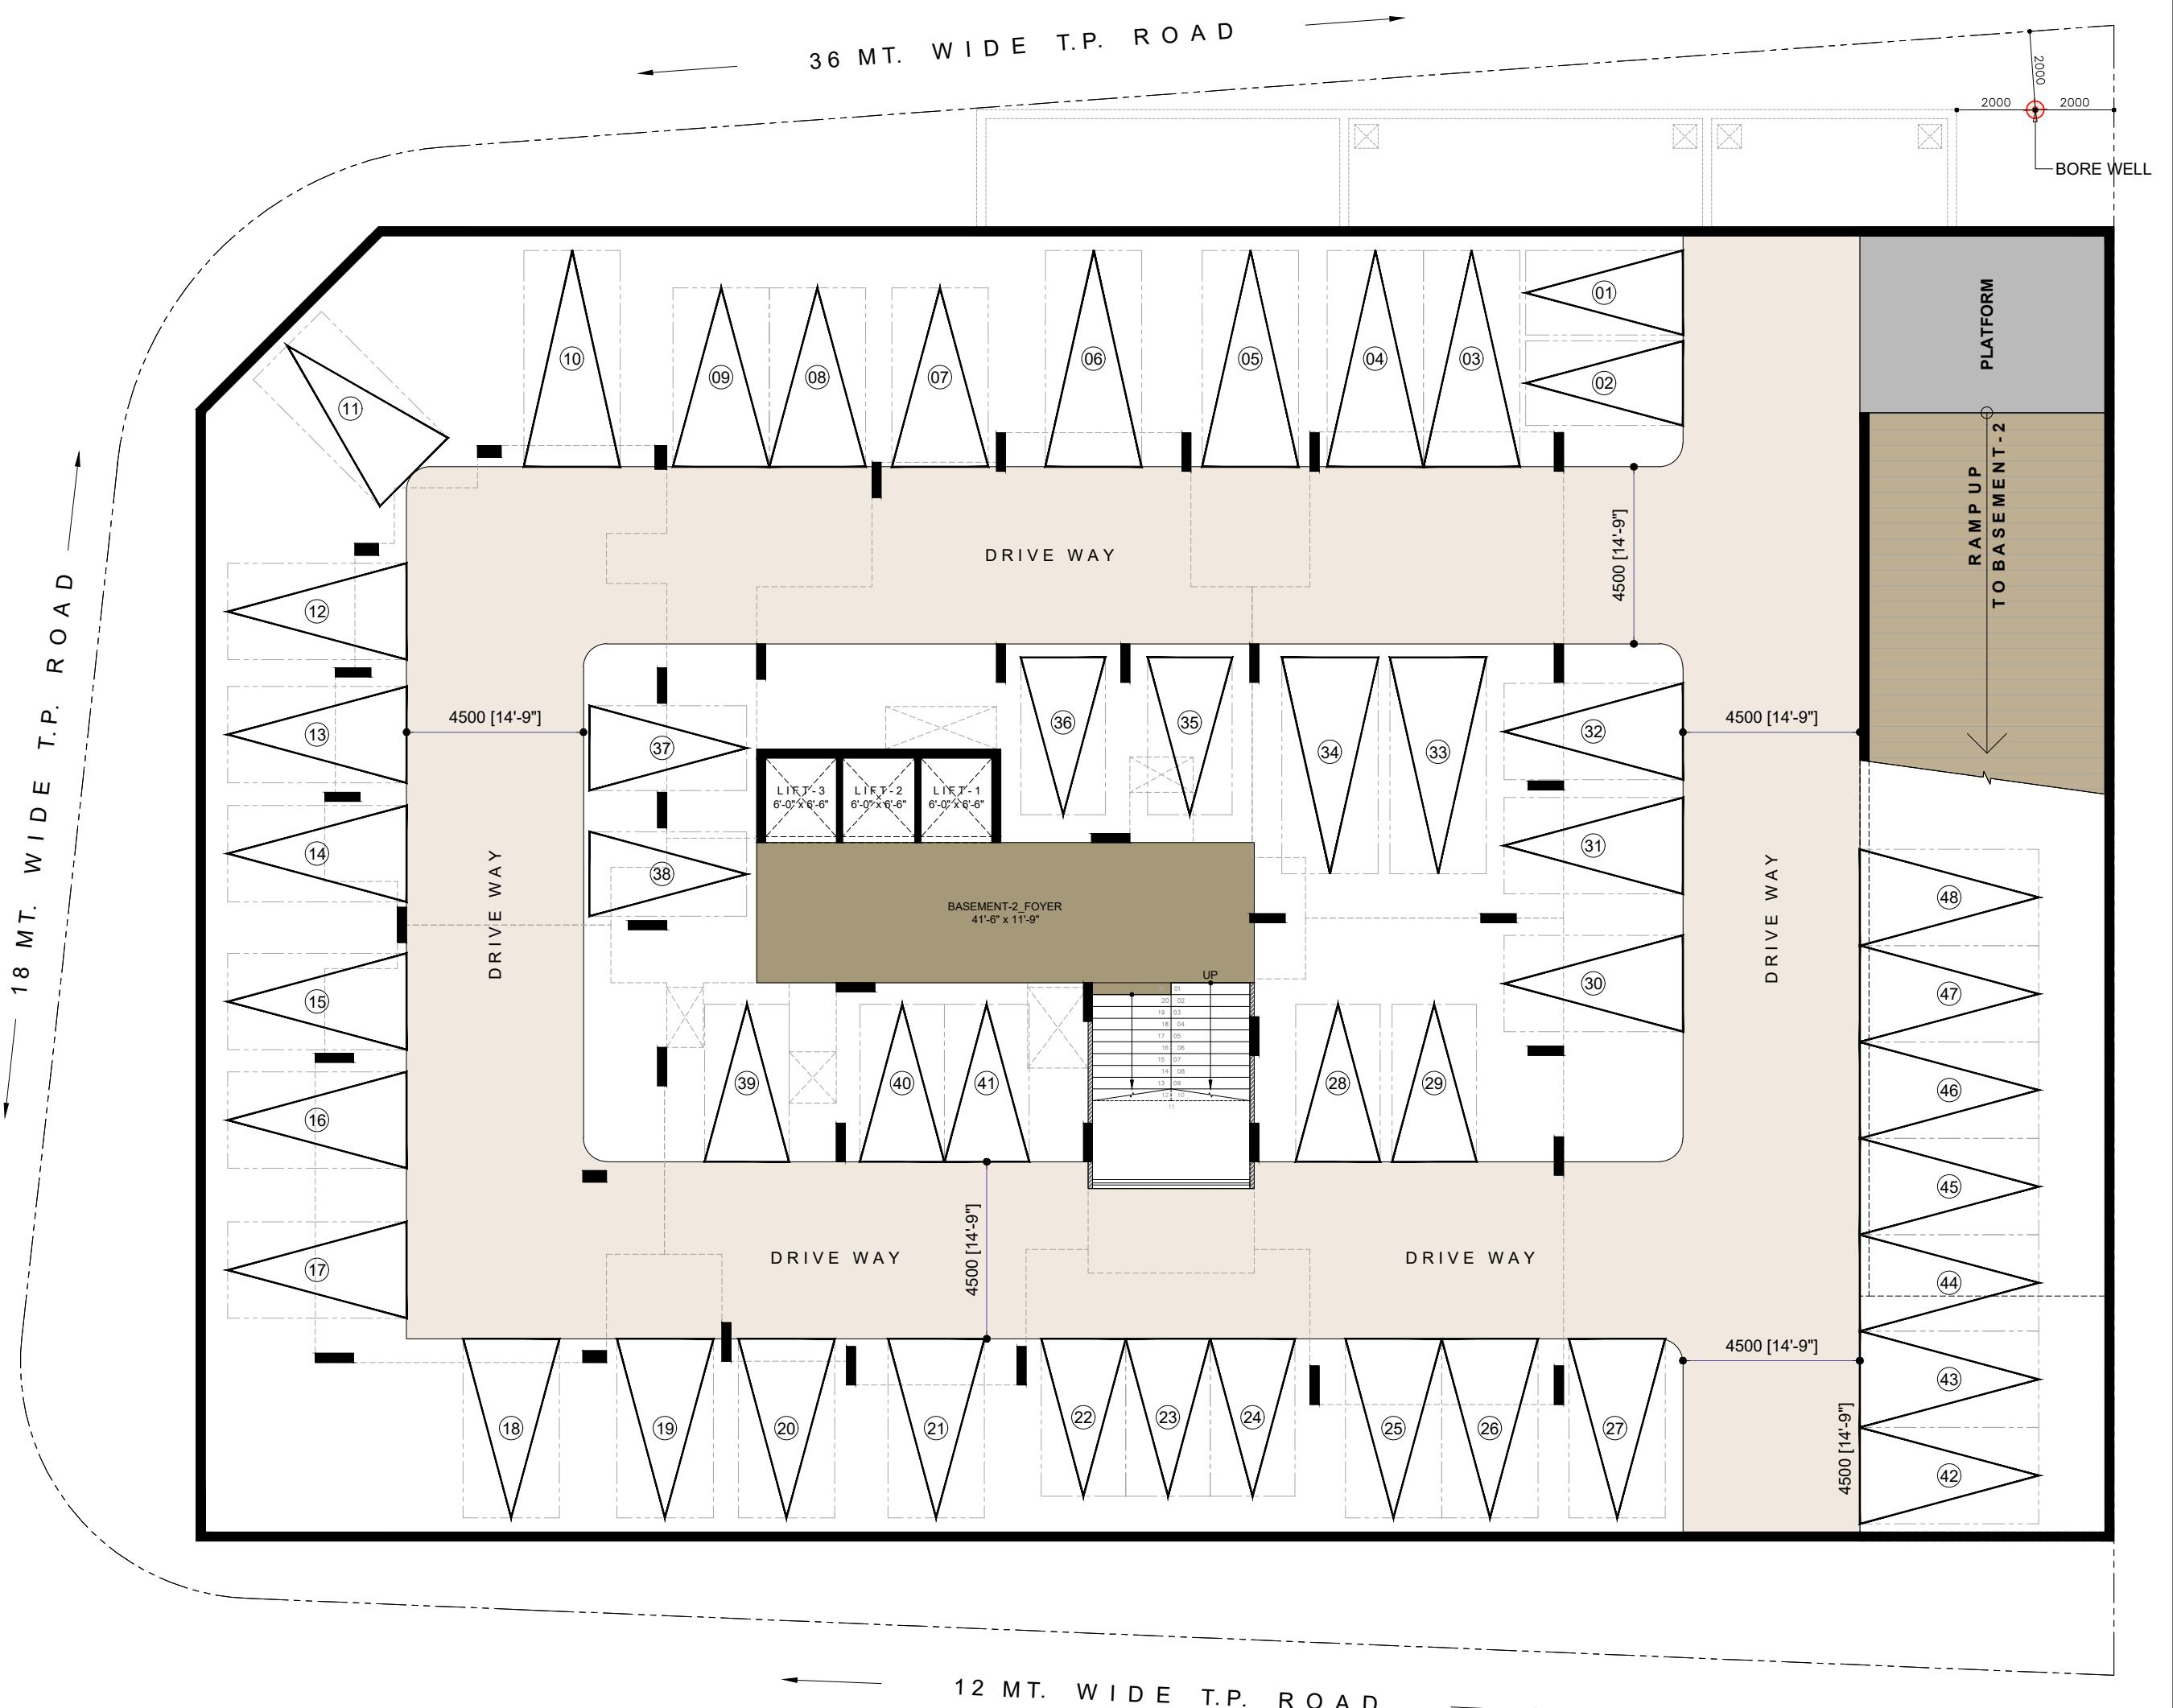

REVISION

DRAWING NAME

PRESENTATION  
BASEMENT-2

DRAWN BY	RV
DATE	20.11.2024
NOT TO SCALE	

A 0 0 2

T.P. 409 B\_F.P. 229

AT ZUNDAL, AHMEDABAD.


ISSUE FOR  
DISCUSSION / CONSTRUCTION  
DATE : 00 / 00 / 2024

A&M DESIGN STUDIO

409, NORTH PLAZA,  
OPP. GOVT. ENGINEERING COLLEGE,  
VISAT - GANDHINAGAR HIGHWAY,  
CHANDIKEDA, AHMEDABAD - 380005  
T : +91 9375 47 15 42  
E : info@aandmstudio.com

## GENERAL NOTES

1. ALL DIMENSION ARE IN MILLIMETERS.
  2. THIS DRAWING IS THE PROPERTY OF A & M DESIGN STUDIO, IS NOT TO BE PRODUCED, COPIED HANDED OVER TO THIRD PARTY OR USED FOR ANY OTHER PURPOSE OTHER THEN FOR WHICH IT IS INTENDED.
  3. ALL DIMENSION SHALL BE VERIFIED ON SITE PRIOR TO START OF WORK, ANY DISCREPANCY SHALL BE BROUGHT TO THE NOTICE OF THE ARCHITECTS.
  4. THE CONTRACTOR MUST CHECK ALL DIMENSIONS AND DETAILS AND BE RESPONSIBLE FOR THE SAME, ANY DISCREPANCY SHALL BE BROUGHT TO THE NOTICE OF THE ARCHITECTS BEFORE EXECUTION.
  5. THIS DRAWING IS TO BE READ AND NOT MEASURED.
  6. THIS DRAWING SHOULD BE READ IN CONJUNCTION WITH RELEVANT WORKING AND DETAILED DRAWINGS.
  7. ALL MENTIONED HEIGHTS ARE WITH RESPECT TO INTERNAL FINISH FLOOR LEVEL FOR
  8. ALL STRUCTURAL DETAILS FOLLOW THE STRUCTURAL DRAWINGS WITH STRUCTURAL NOTIFICATIONS.

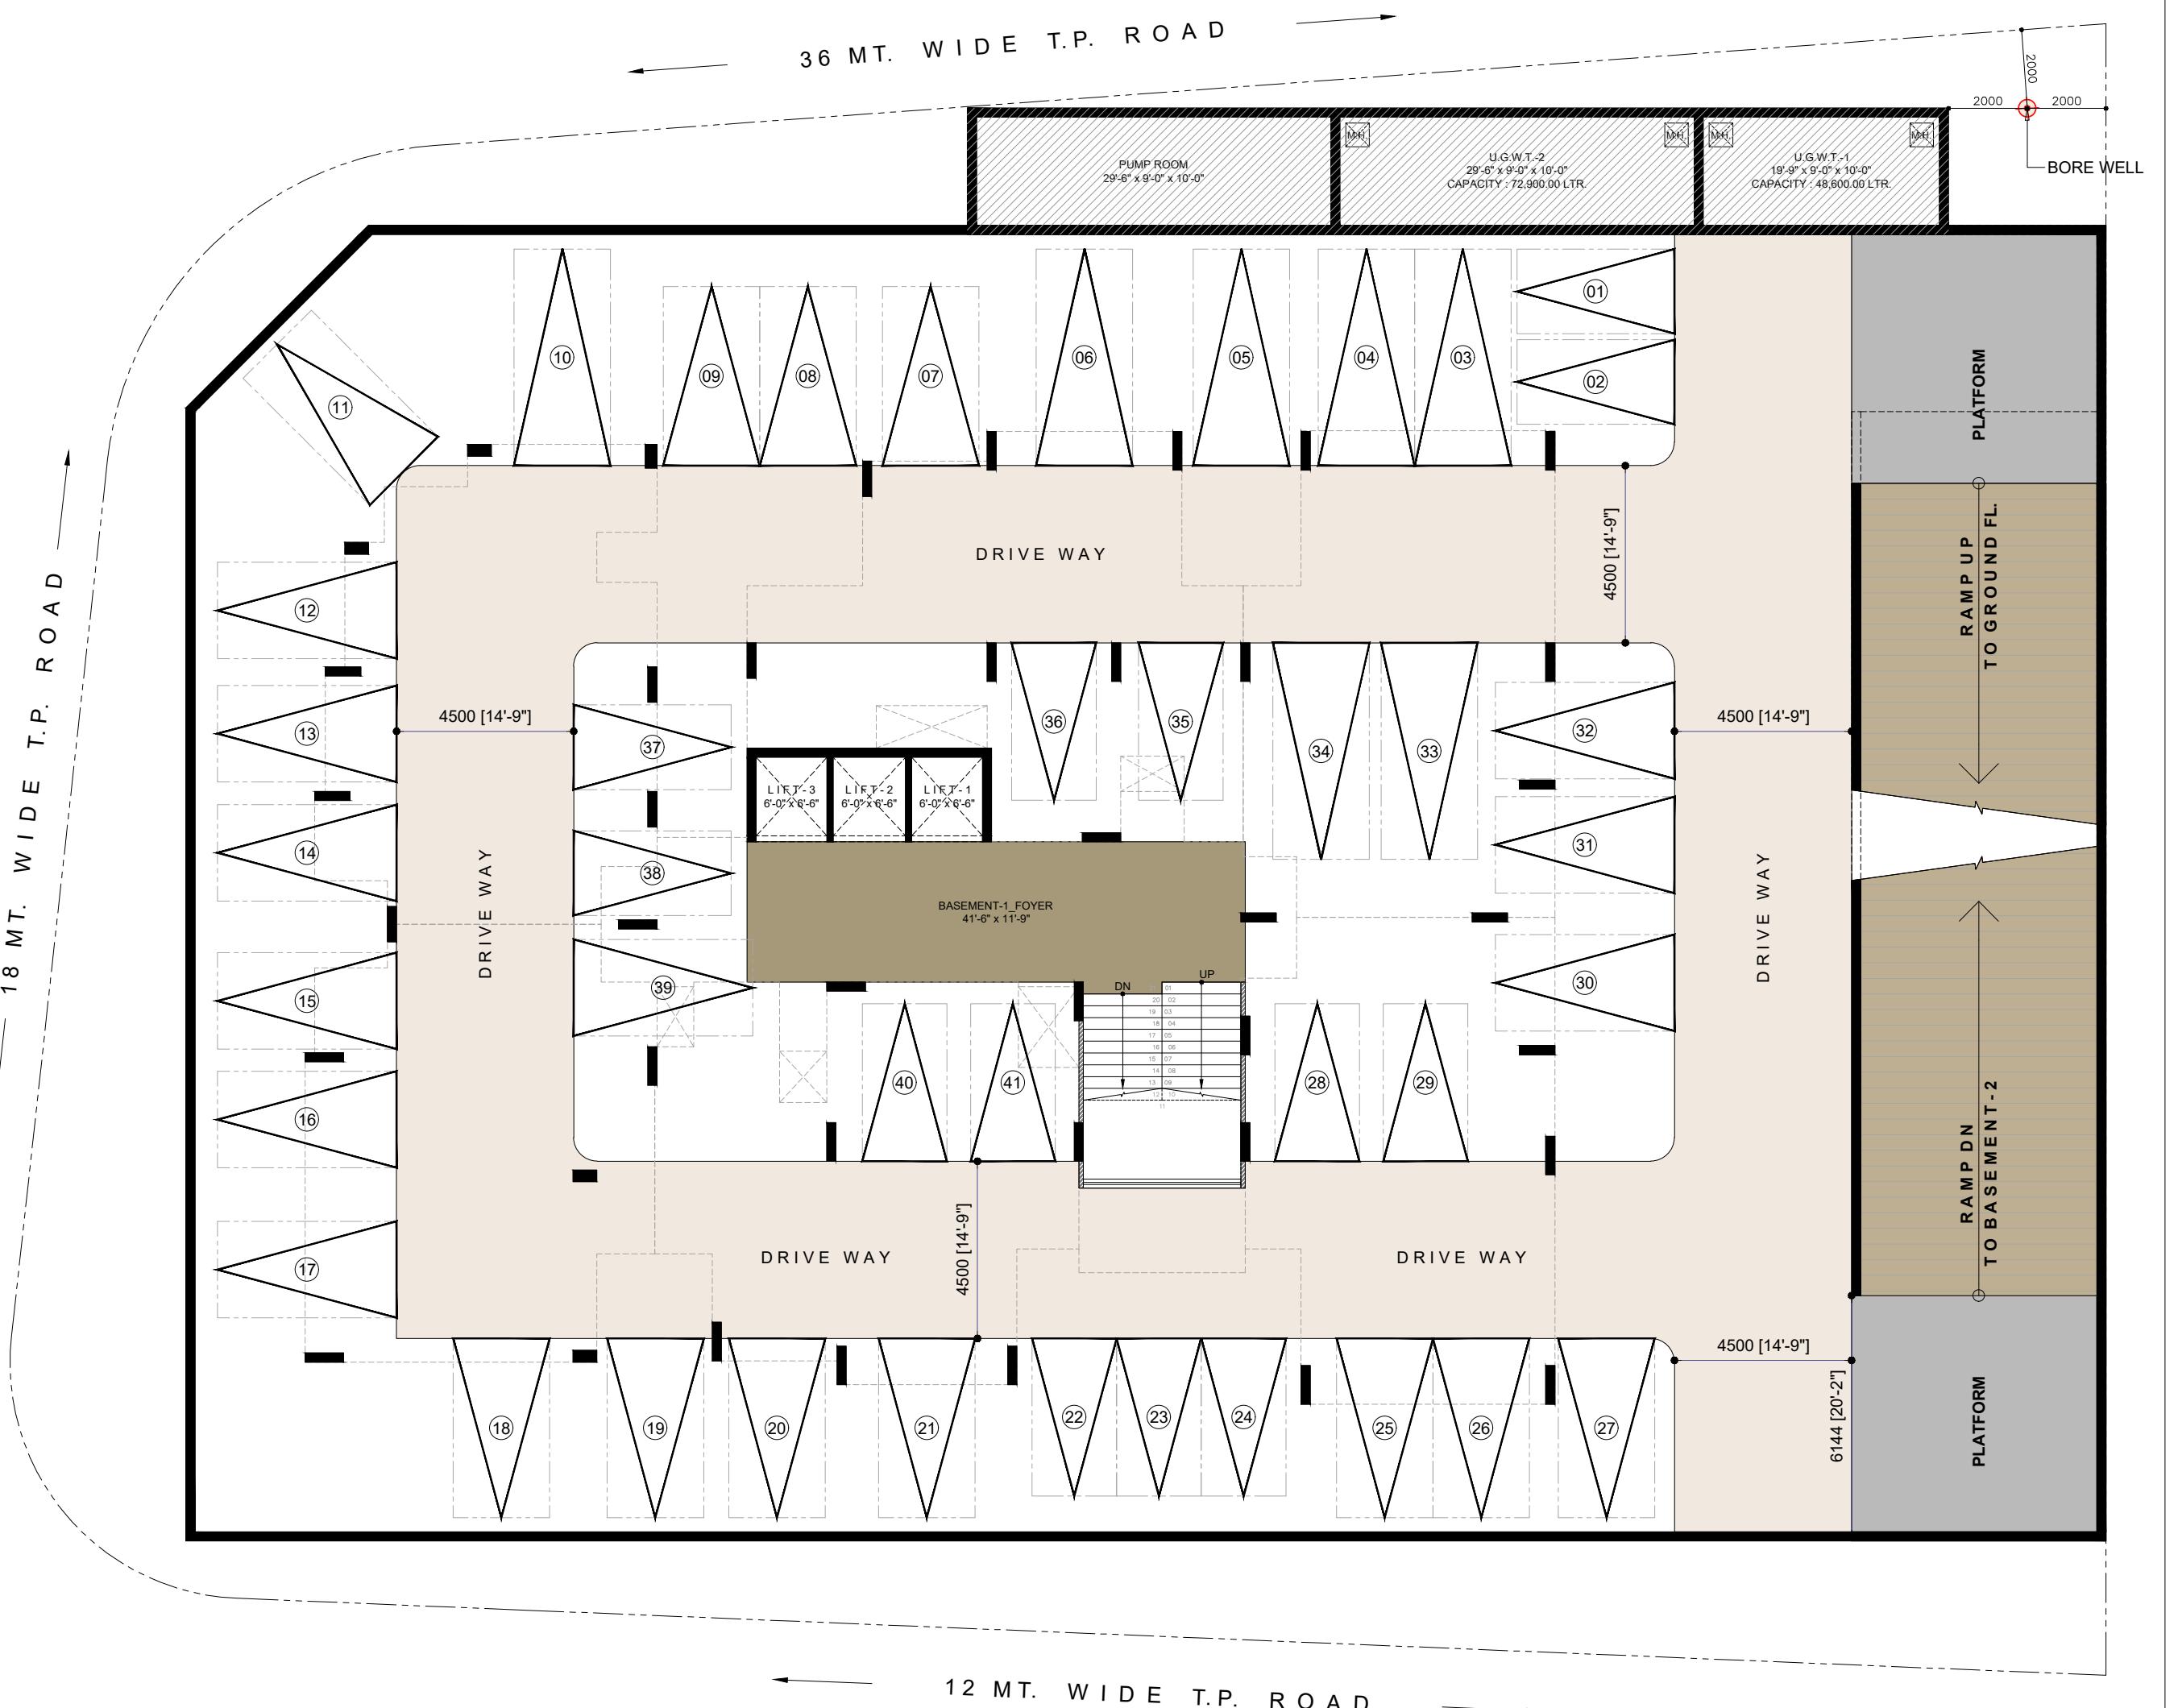

REVISION

DRAWING NAME

PRESENTATION  
BASEMENT-1

DRAWN BY	RV
DATE	20.11.2024
NOT TO SCALE	

A 0 0 1

TP 409 B FP 229

**AT ZUNDAL, AHMEDABAD.**

---

**ISSUE FOR  
DISCUSSION / CONSTRUCTION**

A&M DESIGN STUDIO

400 NORTH PLAZA

409, NORTH PLAZA,  
OPP GOVT ENGINEERING COLLEGE

VISAT - GANDHINAGAR HIGHWAY .

CHANDKHEDA, AHMEDABAD - 380005

T :- +91 9375 47 15 42

E :- info @ aandmstudio.com

## GENERAL NOTES

- ALL DIMENSION ARE IN MILLIMETERS.
- THIS DRAWING IS THE PROPERTY OF A & M DESIGN STUDIO, IS NOT TO BE PRODUCED, COPIED HANDED OVER TO THIRD PARTY OR USED FOR ANY OTHER PURPOSE OTHER THEN FOR WHICH IT IS INTENDED.
- ALL DIMENSION SHALL BE VERIFIED ON SITE PRIOR TO START OF WORK, ANY DISCREPANCY SHALL BE BROUGHT TO THE NOTICE OF THE ARCHITECTS.
- THE CONTRACTOR MUST CHECK ALL DIMENSIONS AND DETAILS AND BE RESPONSIBLE FOR THE SAME, ANY DISCREPANCY SHALL BE BROUGHT TO THE NOTICE OF THE ARCHITECTS BEFORE EXECUTION.
- THIS DRAWING IS TO BE READ AND NOT MEASURED.
- THIS DRAWING SHOULD BE READ IN CONJUNCTION WITH RELEVANT WORKING AND DETAILED DRAWINGS.
- ALL MENTIONED HEIGHTS ARE WITH RESPECT TO INTERNAL FINISH FLOOR LEVEL FOR.
- ALL STRUCTURAL DETAILS FOLLOW THE STRUCTURAL DRAWINGS WITH STRUCTURAL NOTIFICATIONS.



## GENERAL NOTES

- ALL DIMENSION ARE IN MILLIMETERS.
- THIS DRAWING IS THE PROPERTY OF A & M DESIGN STUDIO, IS NOT TO BE PRODUCED, COPIED HANDED OVER TO THIRD PARTY OR USED FOR ANY OTHER PURPOSE OTHER THEN FOR WHICH IT IS INTENDED.
- ALL DIMENSION SHALL BE VERIFIED ON SITE PRIOR TO START OF WORK, ANY DISCREPANCY SHALL BE BROUGHT TO THE NOTICE OF THE ARCHITECTS.
- THE CONTRACTOR MUST CHECK ALL DIMENSIONS AND DETAILS AND BE RESPONSIBLE FOR THE SAME, ANY DISCREPANCY SHALL BE BROUGHT TO THE NOTICE OF THE ARCHITECTS BEFORE EXECUTION.
- THIS DRAWING IS TO BE READ AND NOT MEASURED.
- THIS DRAWING SHOULD BE READ IN CONJUNCTION WITH RELEVANT WORKING AND DETAILED DRAWINGS.
- ALL MENTIONED HEIGHTS ARE WITH RESPECT TO INTERNAL FINISH FLOOR LEVEL FOR.
- ALL STRUCTURAL DETAILS FOLLOW THE STRUCTURAL DRAWINGS WITH STRUCTURAL NOTIFICATIONS.



REVISION

DRAWING NAME

**PRESENTATION  
TYPICAL FLOOR PLAN**

DRAWN BY	RV
DATE	20.11.2024
NOT TO SCALE	

**A 0 2**

**T.P. 409 B\_F.P. 229**

AT ZUNDAL, AHMEDABAD.


ISSUE FOR  
DISCUSSION / CONSTRUCTION  
DATE : 00 / 00 / 2024

**A&M DESIGN STUDIO**

409, NORTH PLAZA,  
OPP. GOVT. ENGINEERING COLLEGE,  
VISAT - GANDHINAGAR HIGHWAY,  
CHANDKHEDA, AHMEDABAD - 380005  
T :- +91 9375 47 15 42  
E :- info@aandmstudio.com


## GENERAL NOTES

- ALL DIMENSION ARE IN MILLIMETERS.
- THIS DRAWING IS THE PROPERTY OF A & M DESIGN STUDIO, IS NOT TO BE PRODUCED, COPIED HANDED OVER TO THIRD PARTY OR USED FOR ANY OTHER PURPOSE OTHER THEN FOR WHICH IT IS INTENDED.
- ALL DIMENSION SHALL BE VERIFIED ON SITE PRIOR TO START OF WORK, ANY DISCREPANCY SHALL BE BROUGHT TO THE NOTICE OF THE ARCHITECTS.
- THE CONTRACTOR MUST CHECK ALL DIMENSIONS AND DETAILS AND BE RESPONSIBLE FOR THE SAME, ANY DISCREPANCY SHALL BE BROUGHT TO THE NOTICE OF THE ARCHITECTS BEFORE EXECUTION.
- THIS DRAWING IS TO BE READ AND NOT MEASURED.
- THIS DRAWING SHOULD BE READ IN CONJUNCTION WITH RELEVANT WORKING AND DETAILED DRAWINGS.
- ALL MENTIONED HEIGHTS ARE WITH RESPECT TO INTERNAL FINISH FLOOR LEVEL FOR.
- ALL STRUCTURAL DETAILS FOLLOW THE STRUCTURAL DRAWINGS WITH STRUCTURAL NOTIFICATIONS.

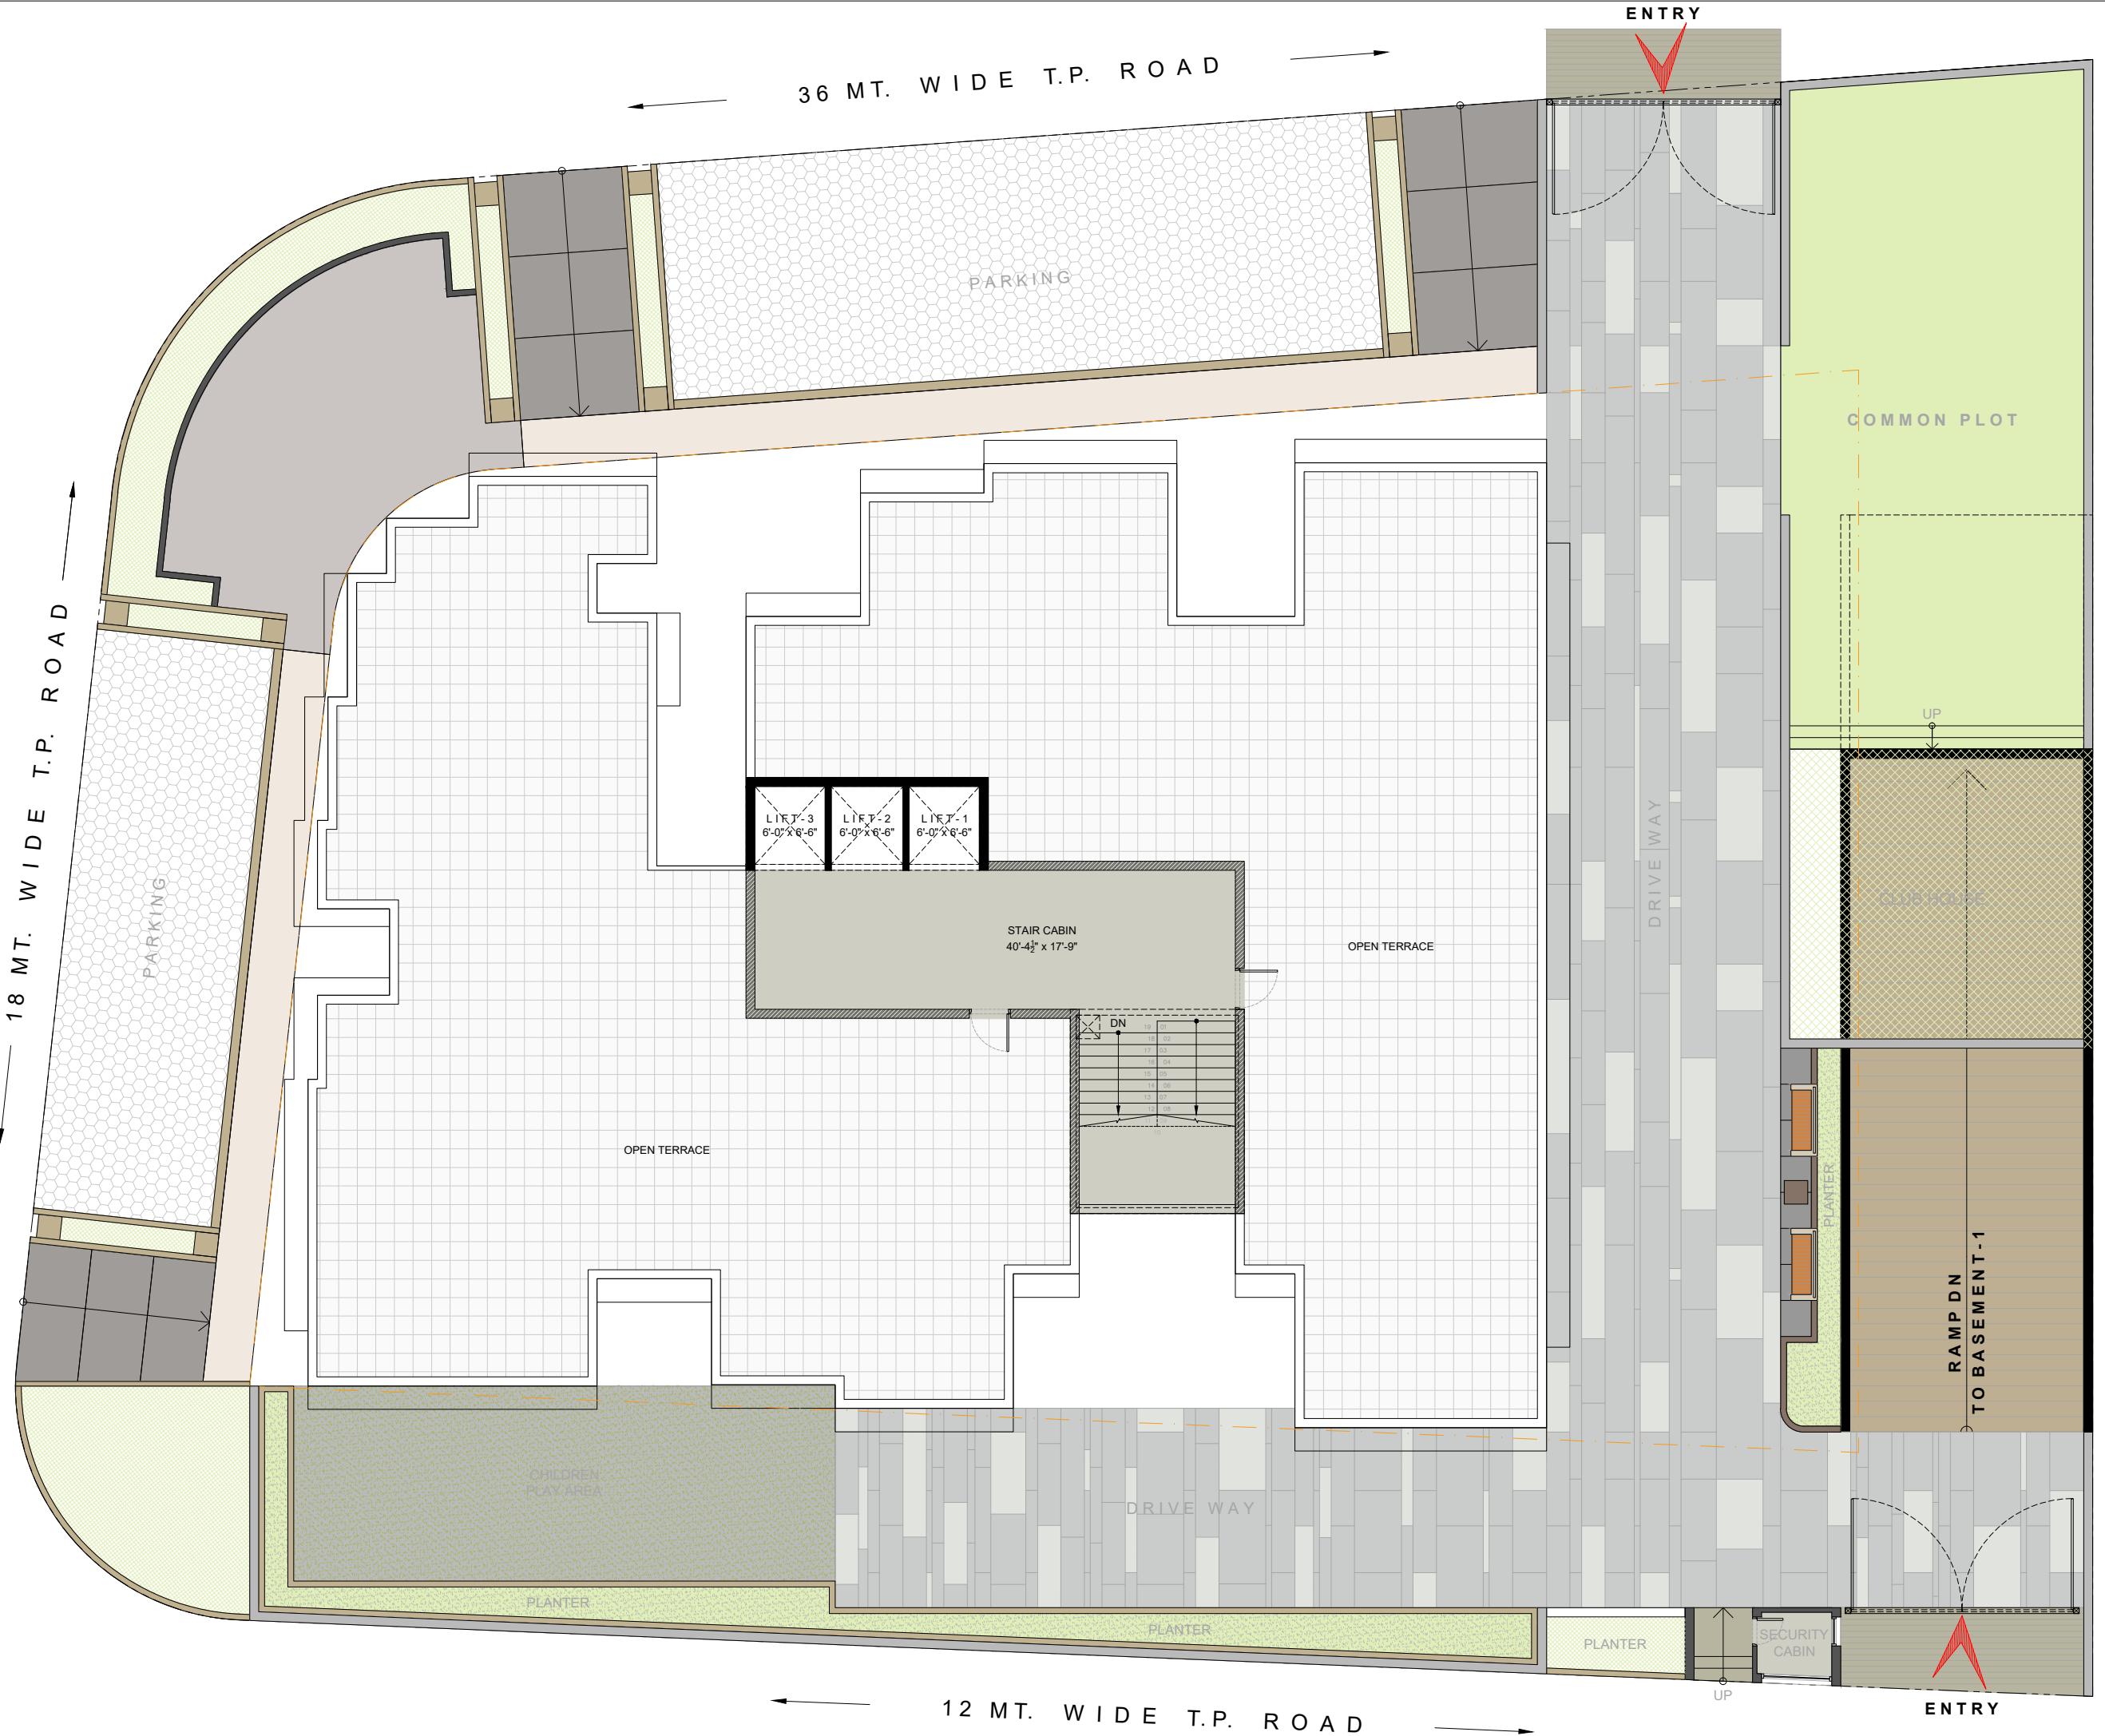

## GENERAL NOTES

- ALL DIMENSION ARE IN MILLIMETERS.
- THIS DRAWING IS THE PROPERTY OF A & M DESIGN STUDIO, IS NOT TO BE PRODUCED, COPIED HANDED OVER TO THIRD PARTY OR USED FOR ANY OTHER PURPOSE OTHER THEN FOR WHICH IT IS INTENDED.
- ALL DIMENSION SHALL BE VERIFIED ON SITE PRIOR TO START OF WORK, ANY DISCREPANCY SHALL BE BROUGHT TO THE NOTICE OF THE ARCHITECTS.
- THE CONTRACTOR MUST CHECK ALL DIMENSIONS AND DETAILS AND BE RESPONSIBLE FOR THE SAME, ANY DISCREPANCY SHALL BE BROUGHT TO THE NOTICE OF THE ARCHITECTS BEFORE EXECUTION.
- THIS DRAWING IS TO BE READ AND NOT MEASURED.
- THIS DRAWING SHOULD BE READ IN CONJUNCTION WITH RELEVANT WORKING AND DETAILED DRAWINGS.
- ALL MENTIONED HEIGHTS ARE WITH RESPECT TO INTERNAL FINISH FLOOR LEVEL FOR.
- ALL STRUCTURAL DETAILS FOLLOW THE STRUCTURAL DRAWINGS WITH STRUCTURAL NOTIFICATIONS.

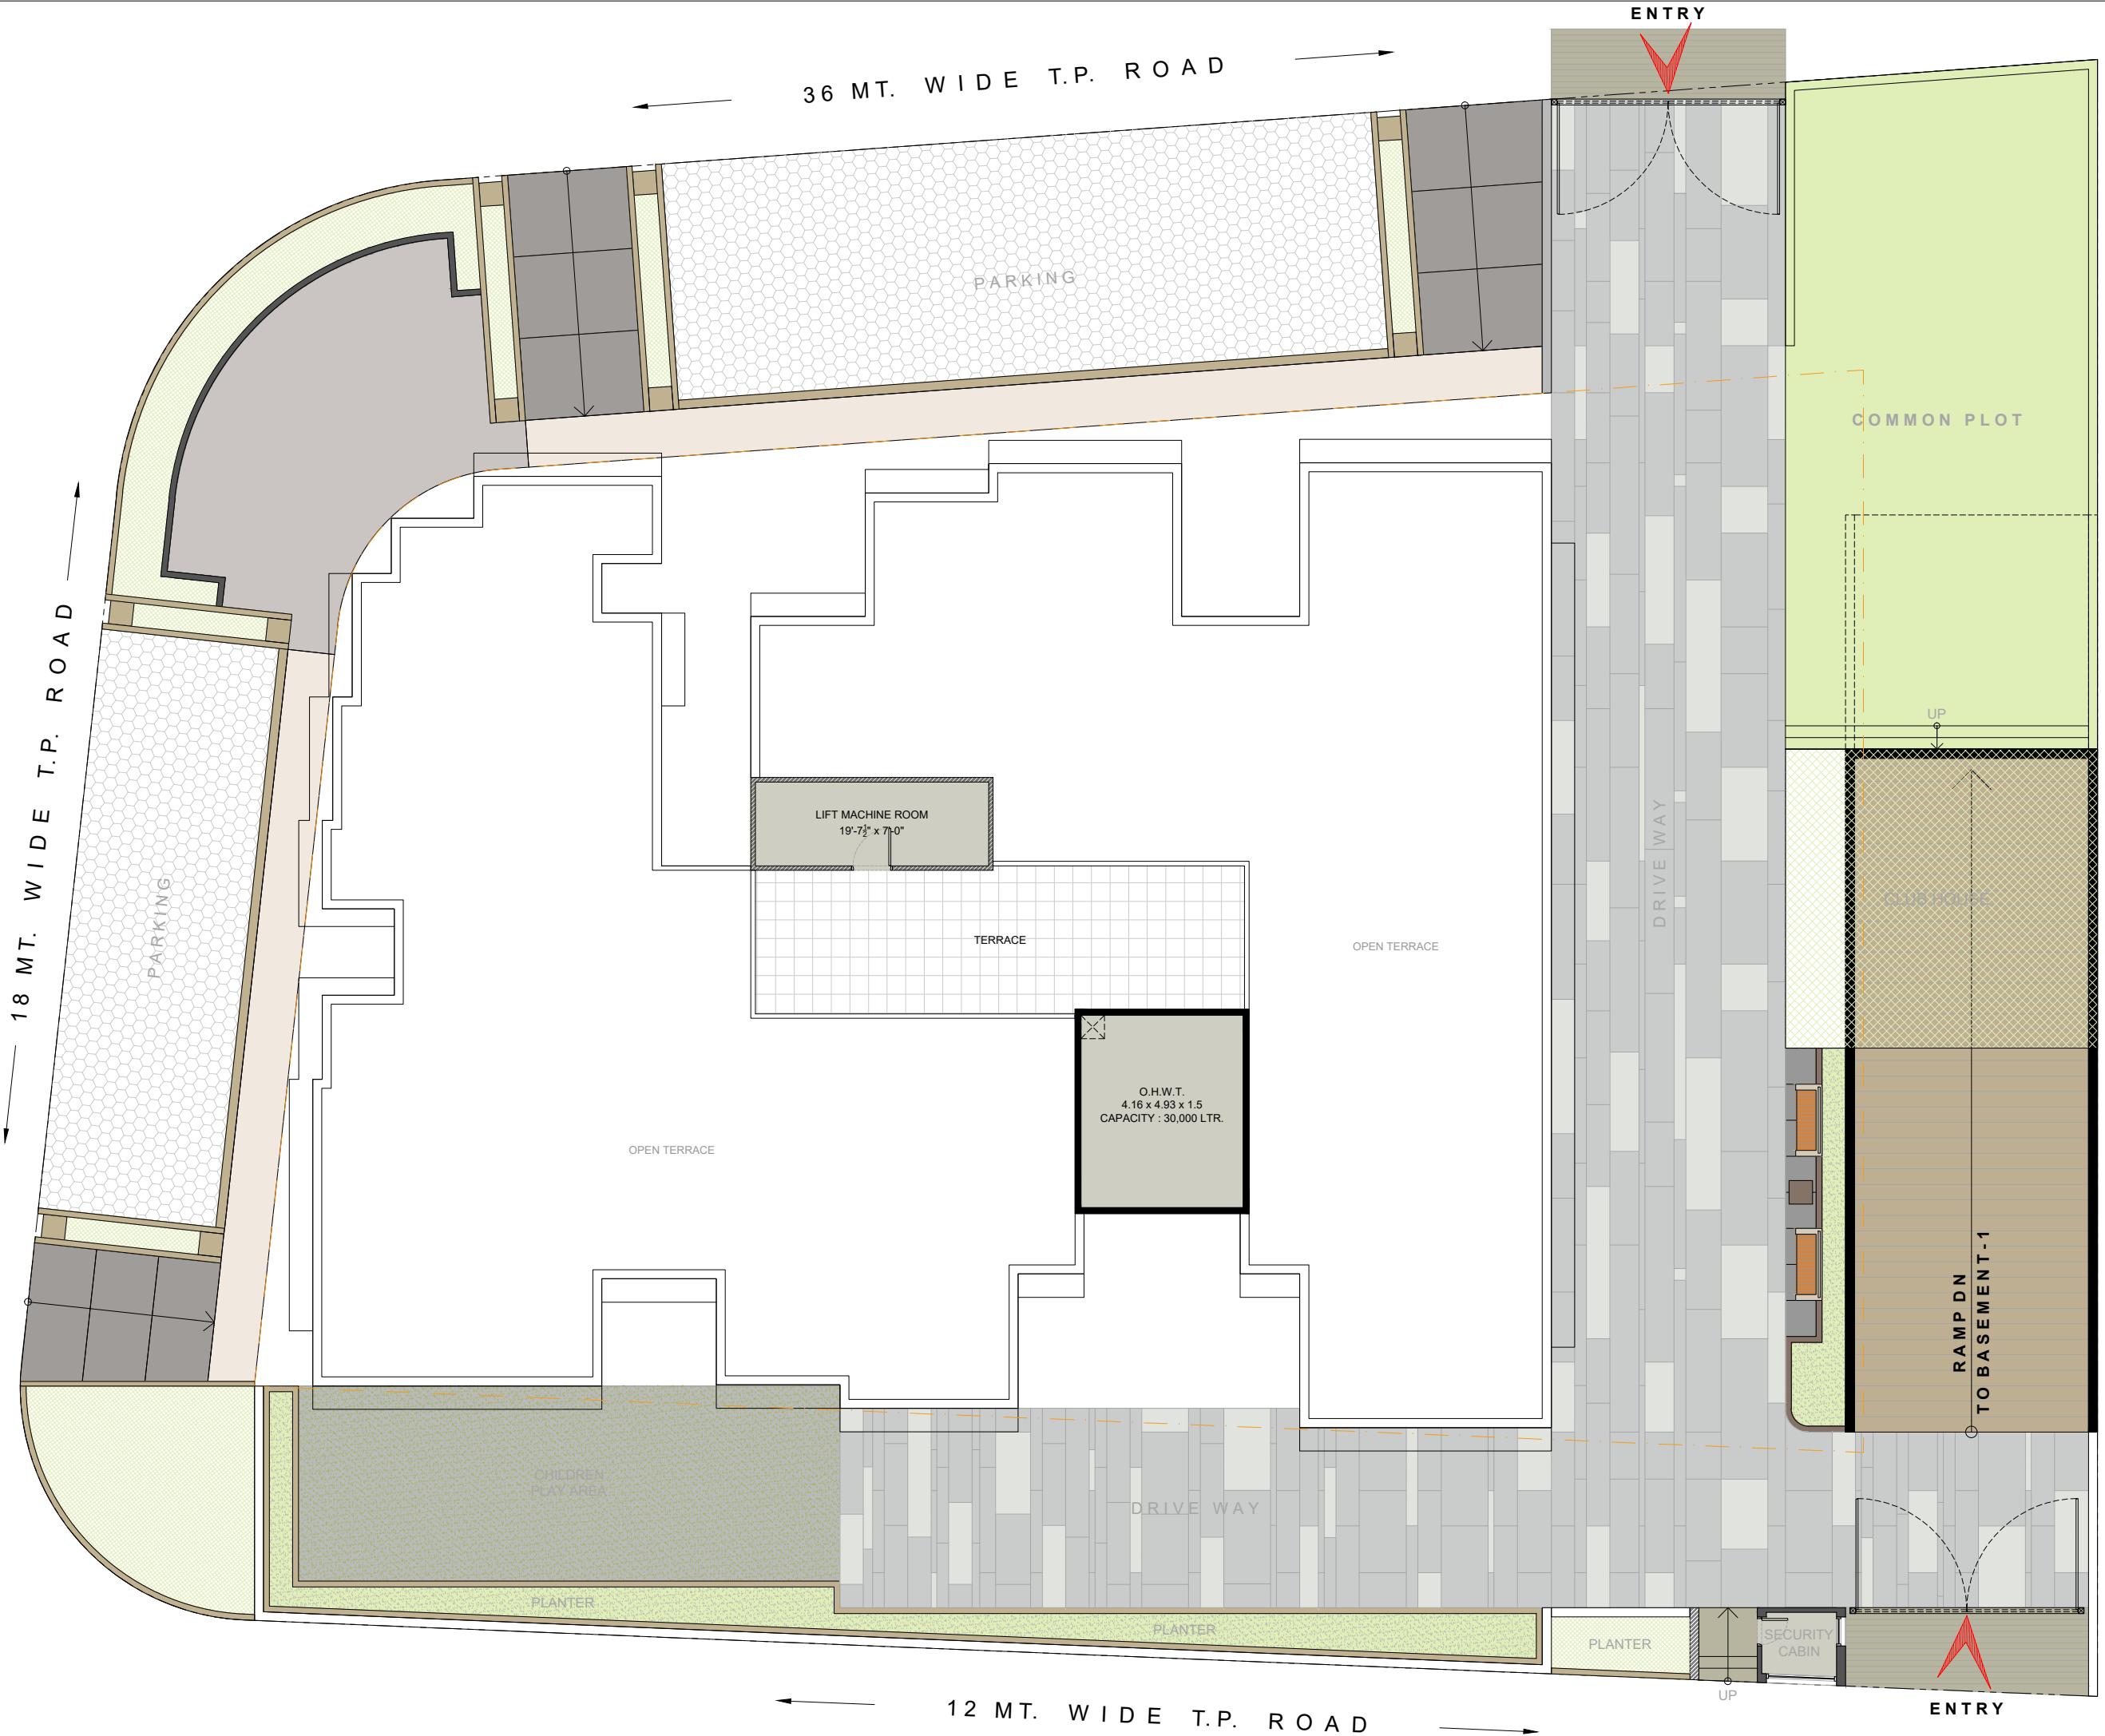

REVISION

DRAWING NAME

**PRESENTATION**  
O.H.W.T. & LIFT M.ROOM PLAN

DRAWN BY	RV
DATE	14.11.2024
NOT TO SCALE	

A 0 4 .

**T.P. 409 B\_F.P. 229**

AT ZUNDAL, AHMEDABAD.


ISSUE FOR  
DISCUSSION / CONSTRUCTION  
DATE : 00 / 00 / 2024

**A&M DESIGN STUDIO**

409, NORTH PLAZA,  
OPP. GOVT. ENGINEERING COLLEGE,  
VISAT - GANDHINAGAR HIGHWAY,  
CHANDKHEDA, AHMEDABAD - 380005  
T :- +91 9375 47 15 42  
E :- info@aandmstudio.com

## GENERAL NOTES

- ALL DIMENSION ARE IN MILLIMETERS.
- THIS DRAWING IS THE PROPERTY OF A & M DESIGN STUDIO, IS NOT TO BE PRODUCED, COPIED HANDED OVER TO THIRD PARTY OR USED FOR ANY OTHER PURPOSE OTHER THEN FOR WHICH IT IS INTENDED.
- ALL DIMENSION SHALL BE VERIFIED ON SITE PRIOR TO START OF WORK, ANY DISCREPANCY SHALL BE BROUGHT TO THE NOTICE OF THE ARCHITECTS.
- THE CONTRACTOR MUST CHECK ALL DIMENSIONS AND DETAILS AND BE RESPONSIBLE FOR THE SAME, ANY DISCREPANCY SHALL BE BROUGHT TO THE NOTICE OF THE ARCHITECTS BEFORE EXECUTION.
- THIS DRAWING IS TO BE READ AND NOT MEASURED.
- THIS DRAWING SHOULD BE READ IN CONJUNCTION WITH RELEVANT WORKING AND DETAILED DRAWINGS.
- ALL MENTIONED HEIGHTS ARE WITH RESPECT TO INTERNAL FINISH FLOOR LEVEL FOR.
- ALL STRUCTURAL DETAILS FOLLOW THE STRUCTURAL DRAWINGS WITH STRUCTURAL NOTIFICATIONS.

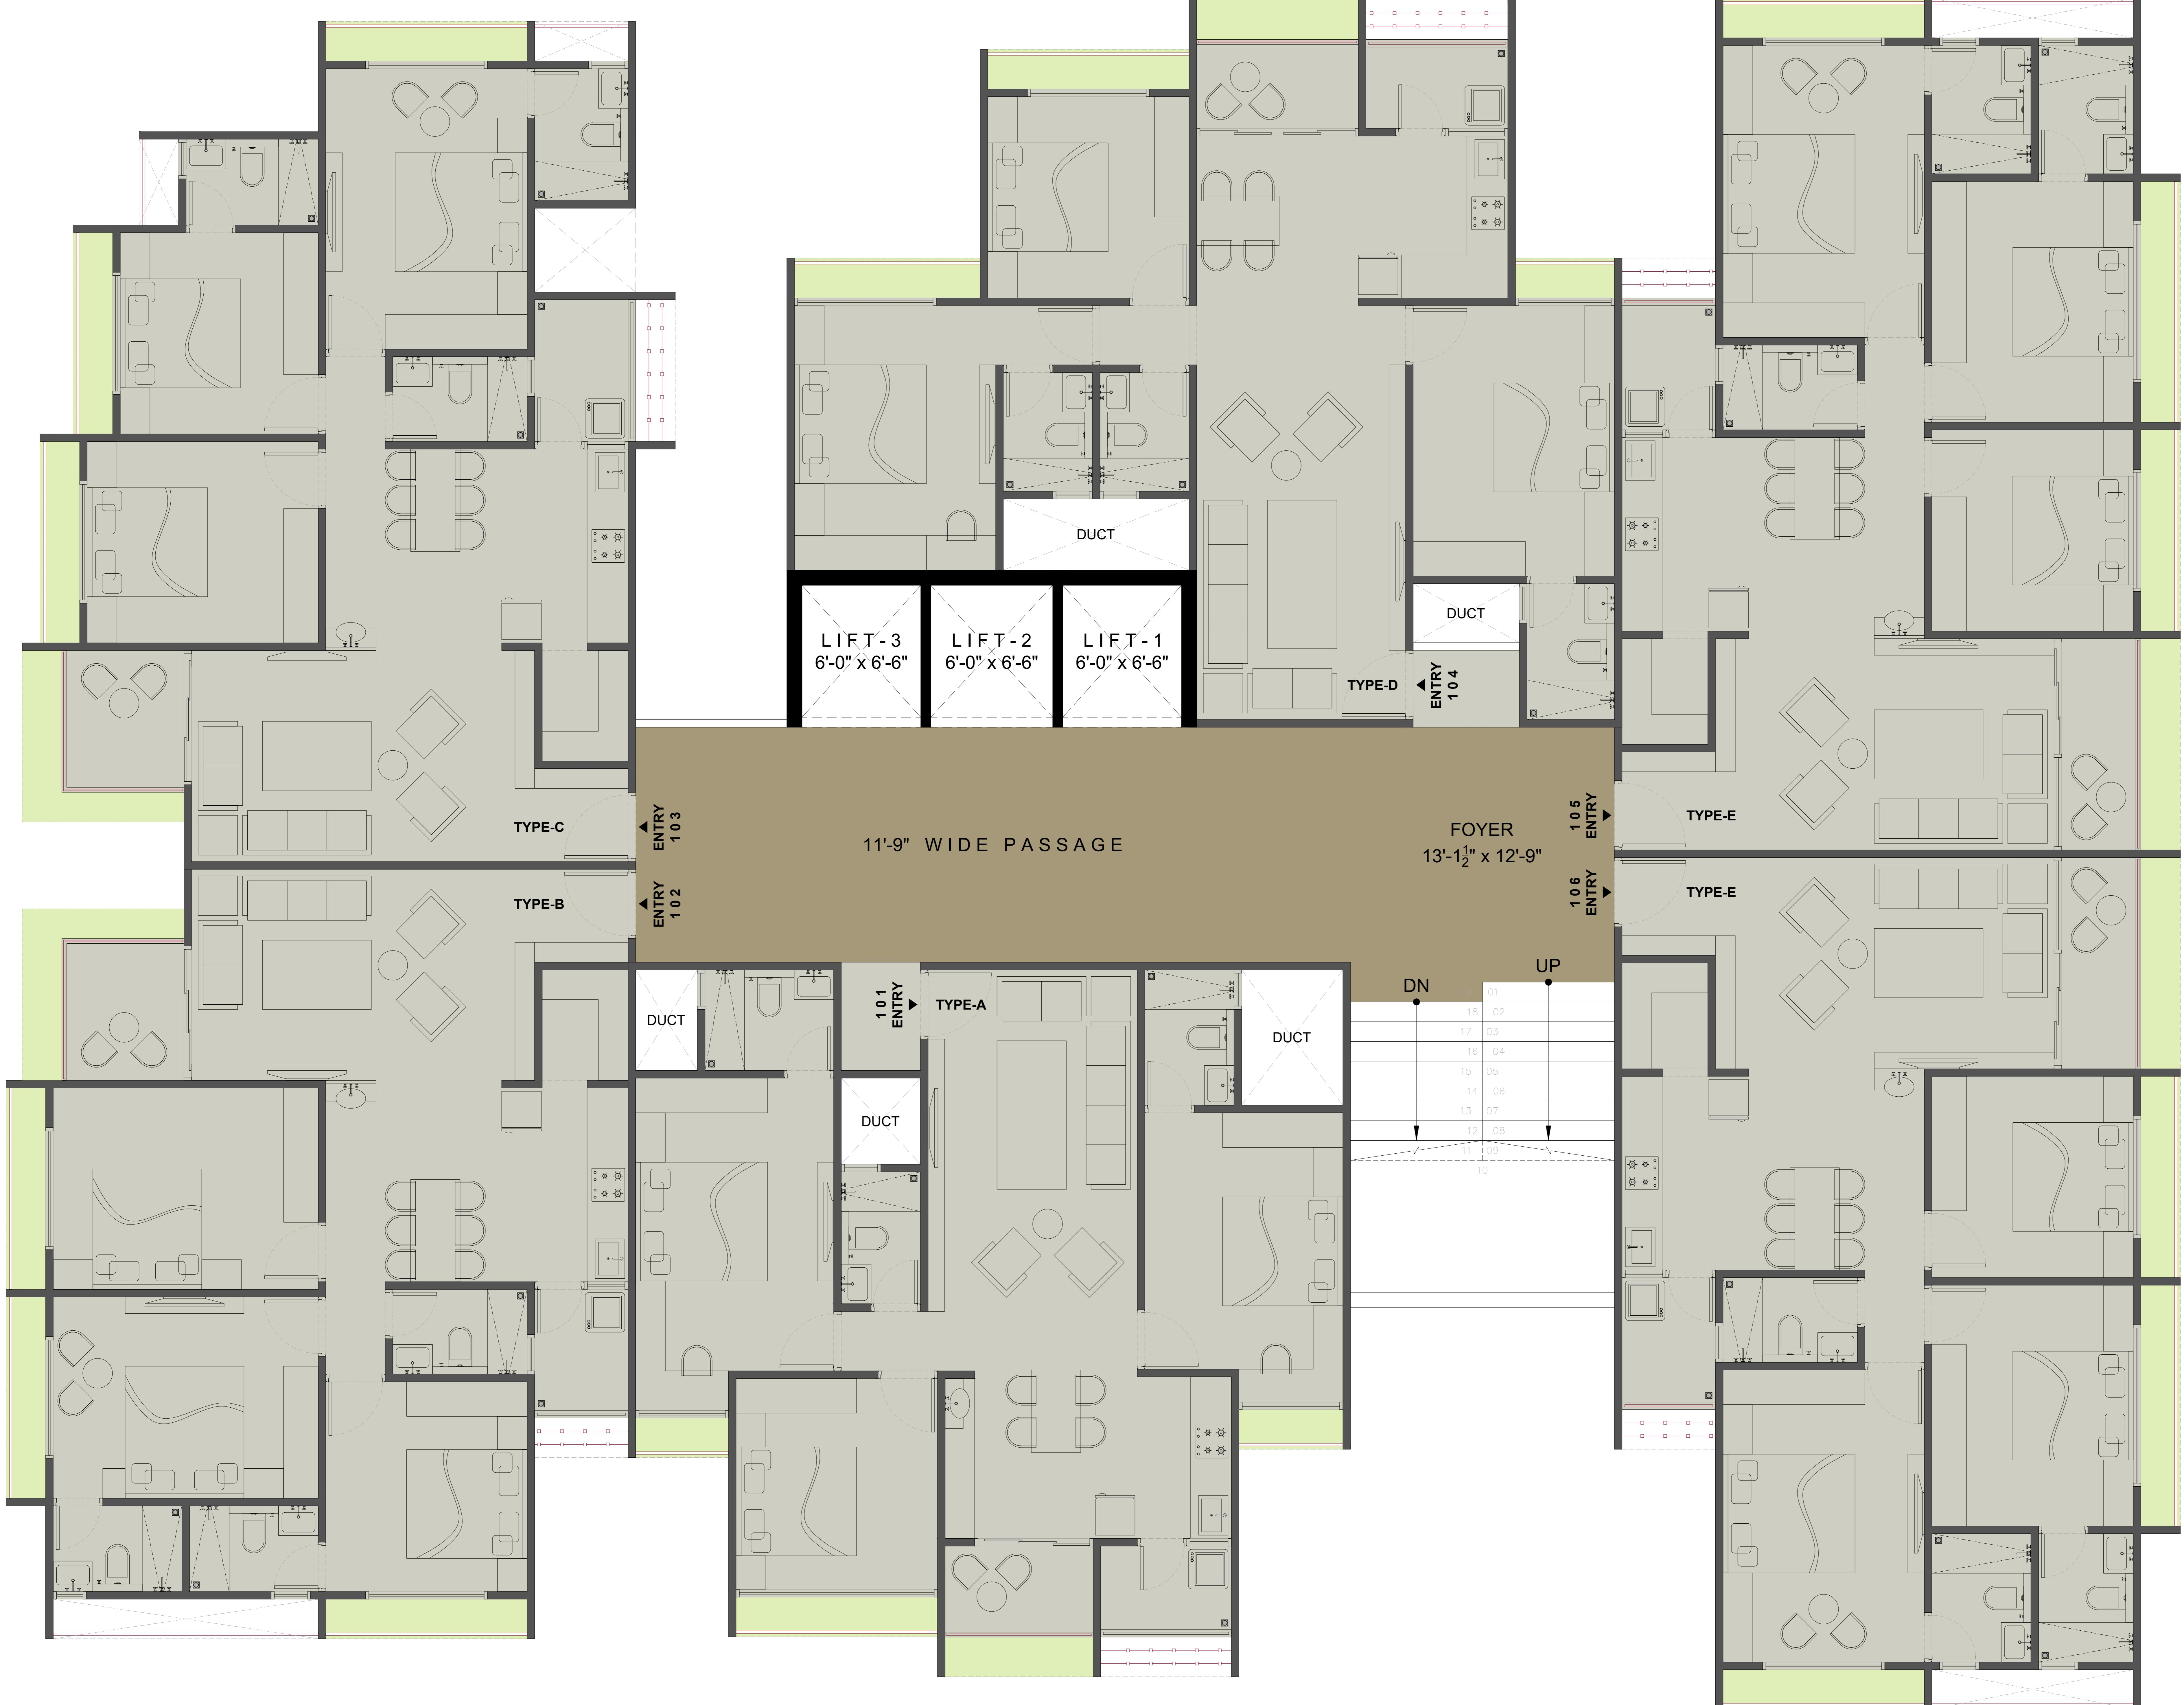

REVISION

DRAWING NAME  
**PRESENTATION  
CLUSTER PLAN**

DRAWN BY **RV**  
DATE **19.11.2024**  
NOT TO SCALE

**A 0 2 a**

**T.P. 409 B\_F.P. 229**

AT ZUNDAL, AHMEDABAD.  
ISSUE FOR  
DISCUSSION / CONSTRUCTION  
DATE : 00 / 00 / 2024

**A&M DESIGN STUDIO**


409, NORTH PLAZA,  
OPP. GOVT. ENGINEERING COLLEGE,  
VISAT - GANDHINAGAR HIGHWAY,  
CHANDIKHEDA, AHMEDABAD - 380005  
T : +91 9375 47 15 42  
E : info@aandmstudio.com

## GENERAL NOTES

- ALL DIMENSION ARE IN MILLIMETERS.
- THIS DRAWING IS THE PROPERTY OF A & M DESIGN STUDIO, IS NOT TO BE PRODUCED, COPIED HANDED OVER TO THIRD PARTY OR USED FOR ANY OTHER PURPOSE OTHER THEN FOR WHICH IT IS INTENDED.
- ALL DIMENSION SHALL BE VERIFIED ON SITE PRIOR TO START OF WORK, ANY DISCREPANCY SHALL BE BROUGHT TO THE NOTICE OF THE ARCHITECTS.
- THE CONTRACTOR MUST CHECK ALL DIMENSIONS AND DETAILS AND BE RESPONSIBLE FOR THE SAME, ANY DISCREPANCY SHALL BE BROUGHT TO THE NOTICE OF THE ARCHITECTS BEFORE EXECUTION.
- THIS DRAWING IS TO BE READ AND NOT MEASURED.
- THIS DRAWING SHOULD BE READ IN CONJUNCTION WITH RELEVANT WORKING AND DETAILED DRAWINGS.
- ALL MENTIONED HEIGHTS ARE WITH RESPECT TO INTERNAL FINISH FLOOR LEVEL FOR.
- ALL STRUCTURAL DETAILS FOLLOW THE STRUCTURAL DRAWINGS WITH STRUCTURAL NOTIFICATIONS.



## KEY-PLAN

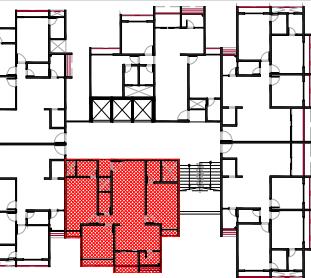

## REVISION

## DRAWING NAME

**PRESENTATION**  
**TYPE-A\_UNIT PLAN**

DRAWN BY	RV
DATE	19.11.2024
NOT TO SCALE	

A 0 2 a

T.P. 409 B\_F.P. 229

AT ZUNDAL, AHMEDABAD.

ISSUE FOR  
DISCUSSION / CONSTRUCTION  
DATE : 00 / 00 / 2024

## A&M DESIGN STUDIO


409, NORTH PLAZA,  
OPP. GOVT. ENGINEERING COLLEGE,  
VISAT - GANDHINAGAR HIGHWAY,  
CHANDIKHEDA, AHMEDABAD - 380005  
T :- +91 9375 47 15 42  
E :- info@aandmstudio.com

**3 BHK (TYPE-A)**

**S. BUILT UP AREA : 211 SQ.YRD.**

## GENERAL NOTES

- ALL DIMENSION ARE IN MILLIMETERS.
- THIS DRAWING IS THE PROPERTY OF A & M DESIGN STUDIO, IS NOT TO BE PRODUCED, COPIED HANDED OVER TO THIRD PARTY OR USED FOR ANY OTHER PURPOSE OTHER THEN FOR WHICH IT IS INTENDED.
- ALL DIMENSION SHALL BE VERIFIED ON SITE PRIOR TO START OF WORK, ANY DISCREPANCY SHALL BE BROUGHT TO THE NOTICE OF THE ARCHITECTS.
- THE CONTRACTOR MUST CHECK ALL DIMENSIONS AND DETAILS AND BE RESPONSIBLE FOR THE SAME, ANY DISCREPANCY SHALL BE BROUGHT TO THE NOTICE OF THE ARCHITECTS BEFORE EXECUTION.
- THIS DRAWING IS TO BE READ AND NOT MEASURED.
- THIS DRAWING SHOULD BE READ IN CONJUNCTION WITH RELEVANT WORKING AND DETAILED DRAWINGS.
- ALL MENTIONED HEIGHTS ARE WITH RESPECT TO INTERNAL FINISH FLOOR LEVEL FOR.
- ALL STRUCTURAL DETAILS FOLLOW THE STRUCTURAL DRAWINGS WITH STRUCTURAL NOTIFICATIONS.

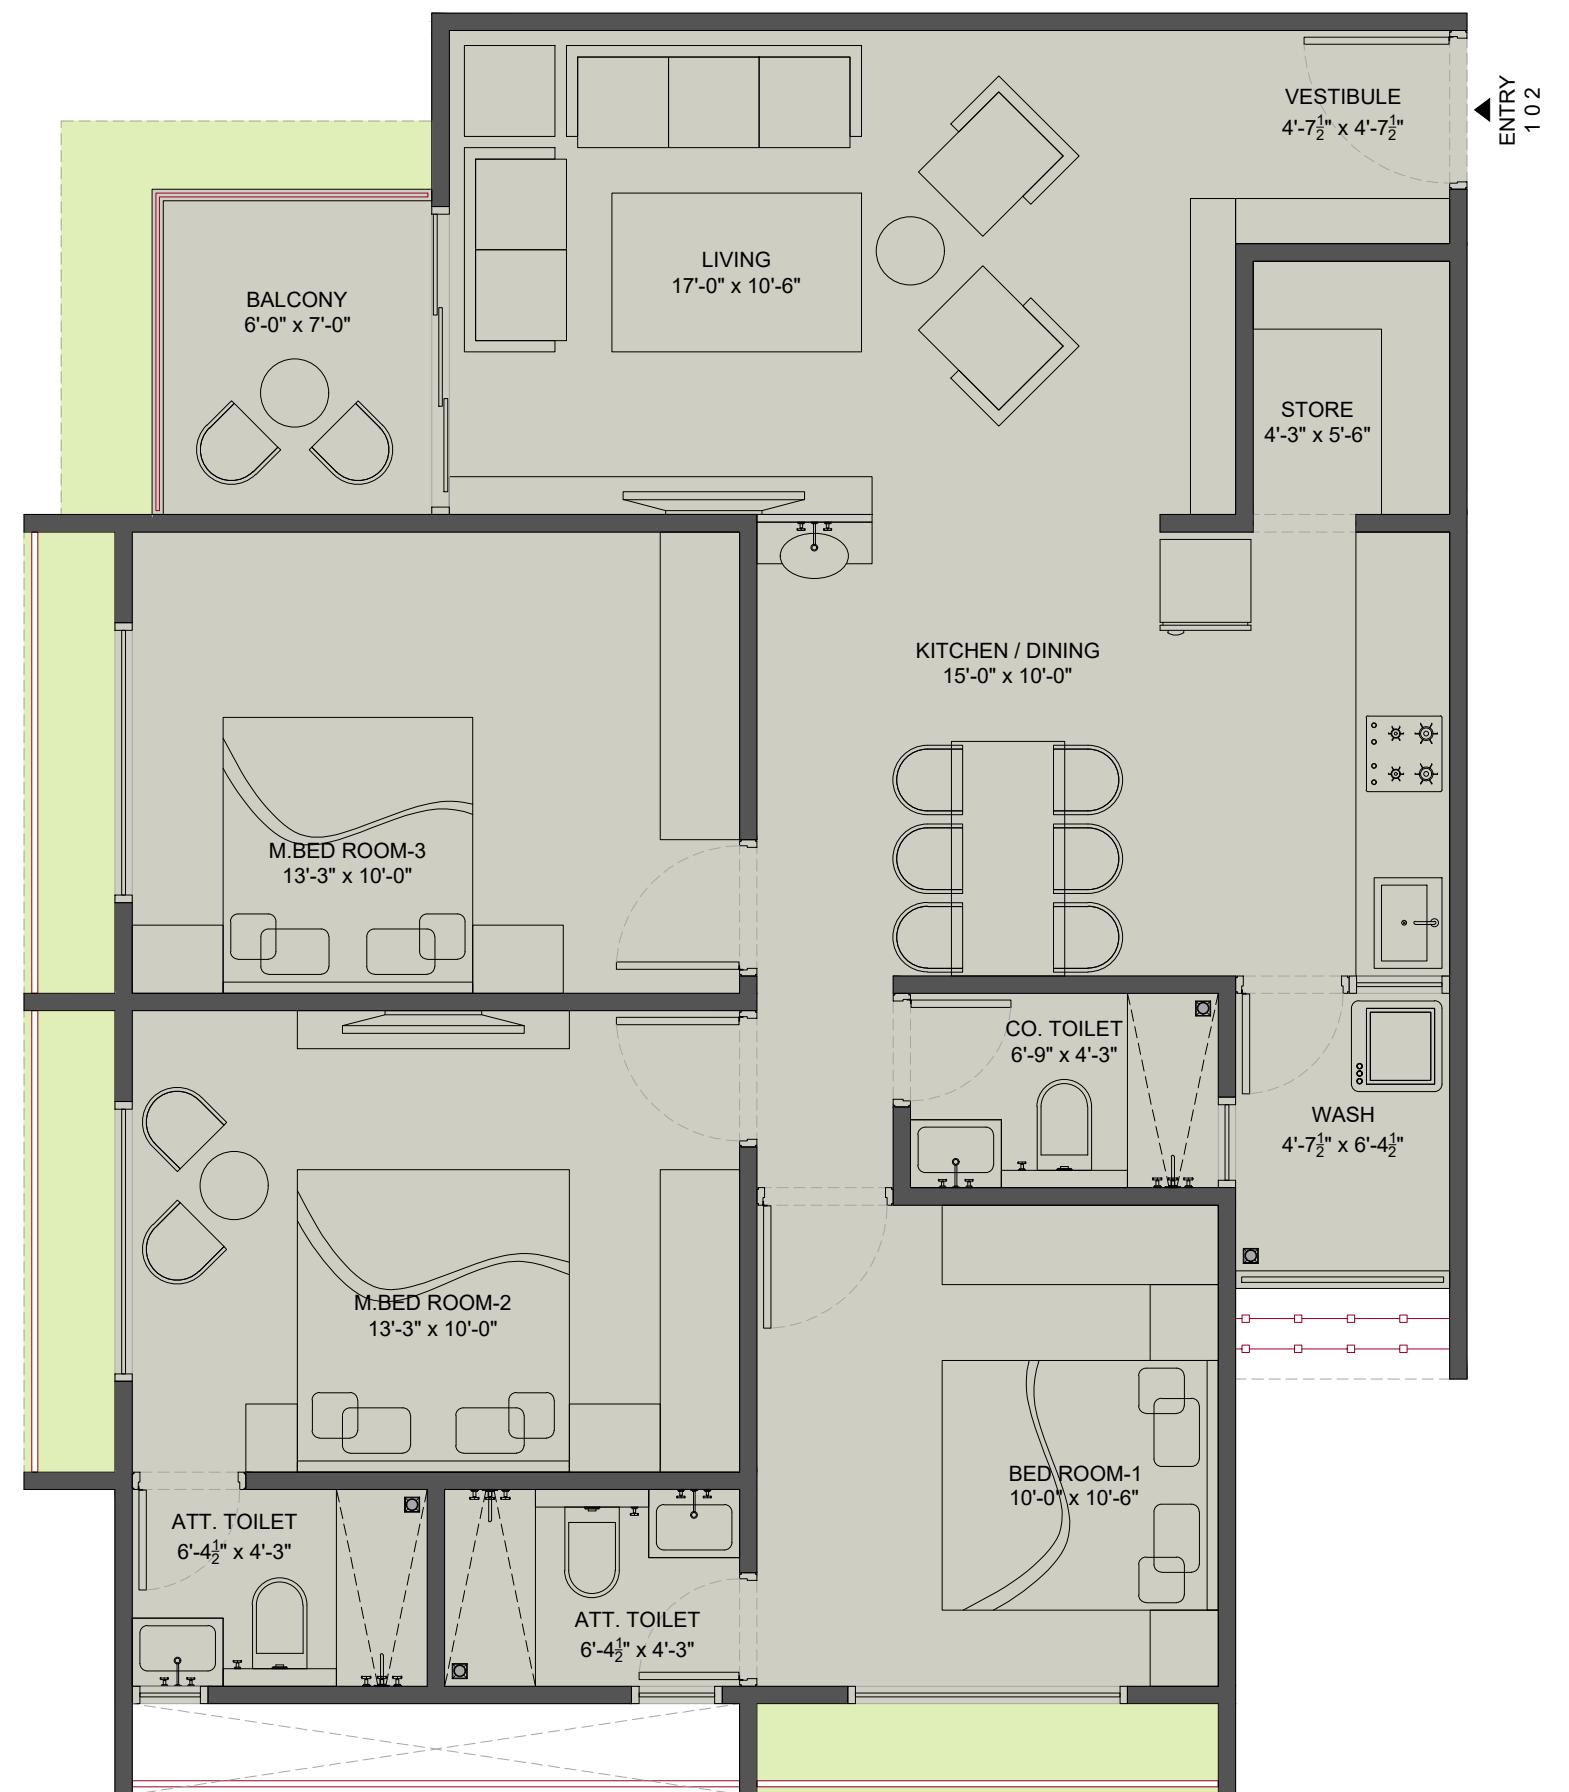

**3 BHK (TYPE-B)**

**S. BUILT UP AREA : 211 SQ.YRD.**

## KEY-PLAN



## REVISION

## DRAWING NAME

**PRESNTATION  
TYPE-B\_UNIT PLAN**

DRAWN BY	RV
DATE	19.11.2024
NOT TO SCALE	

A	0	2	b
---	---	---	---

**T.P. 409 B\_F.P. 229**

AT ZUNDAL, AHMEDABAD.


ISSUE FOR  
DISCUSSION / CONSTRUCTION  
DATE : 00 / 00 / 2024

## A&M DESIGN STUDIO

409, NORTH PLAZA,  
OPP. GOVT. ENGINEERING COLLEGE,  
VISAT - GANDHINAGAR HIGHWAY,  
CHANDIKHEDA, AHMEDABAD - 380005  
T :- +91 9375 47 15 42  
E :- info@aandmstudio.com

## GENERAL NOTES

- ALL DIMENSION ARE IN MILLIMETERS.
- THIS DRAWING IS THE PROPERTY OF A & M DESIGN STUDIO, IS NOT TO BE PRODUCED, COPIED HANDED OVER TO THIRD PARTY OR USED FOR ANY OTHER PURPOSE OTHER THEN FOR WHICH IT IS INTENDED.
- ALL DIMENSION SHALL BE VERIFIED ON SITE PRIOR TO START OF WORK, ANY DISCREPANCY SHALL BE BROUGHT TO THE NOTICE OF THE ARCHITECTS.
- THE CONTRACTOR MUST CHECK ALL DIMENSIONS AND DETAILS AND BE RESPONSIBLE FOR THE SAME, ANY DISCREPANCY SHALL BE BROUGHT TO THE NOTICE OF THE ARCHITECTS BEFORE EXECUTION.
- THIS DRAWING IS TO BE READ AND NOT MEASURED.
- THIS DRAWING SHOULD BE READ IN CONJUNCTION WITH RELEVANT WORKING AND DETAILED DRAWINGS.
- ALL MENTIONED HEIGHTS ARE WITH RESPECT TO INTERNAL FINISH FLOOR LEVEL FOR.
- ALL STRUCTURAL DETAILS FOLLOW THE STRUCTURAL DRAWINGS WITH STRUCTURAL NOTIFICATIONS.

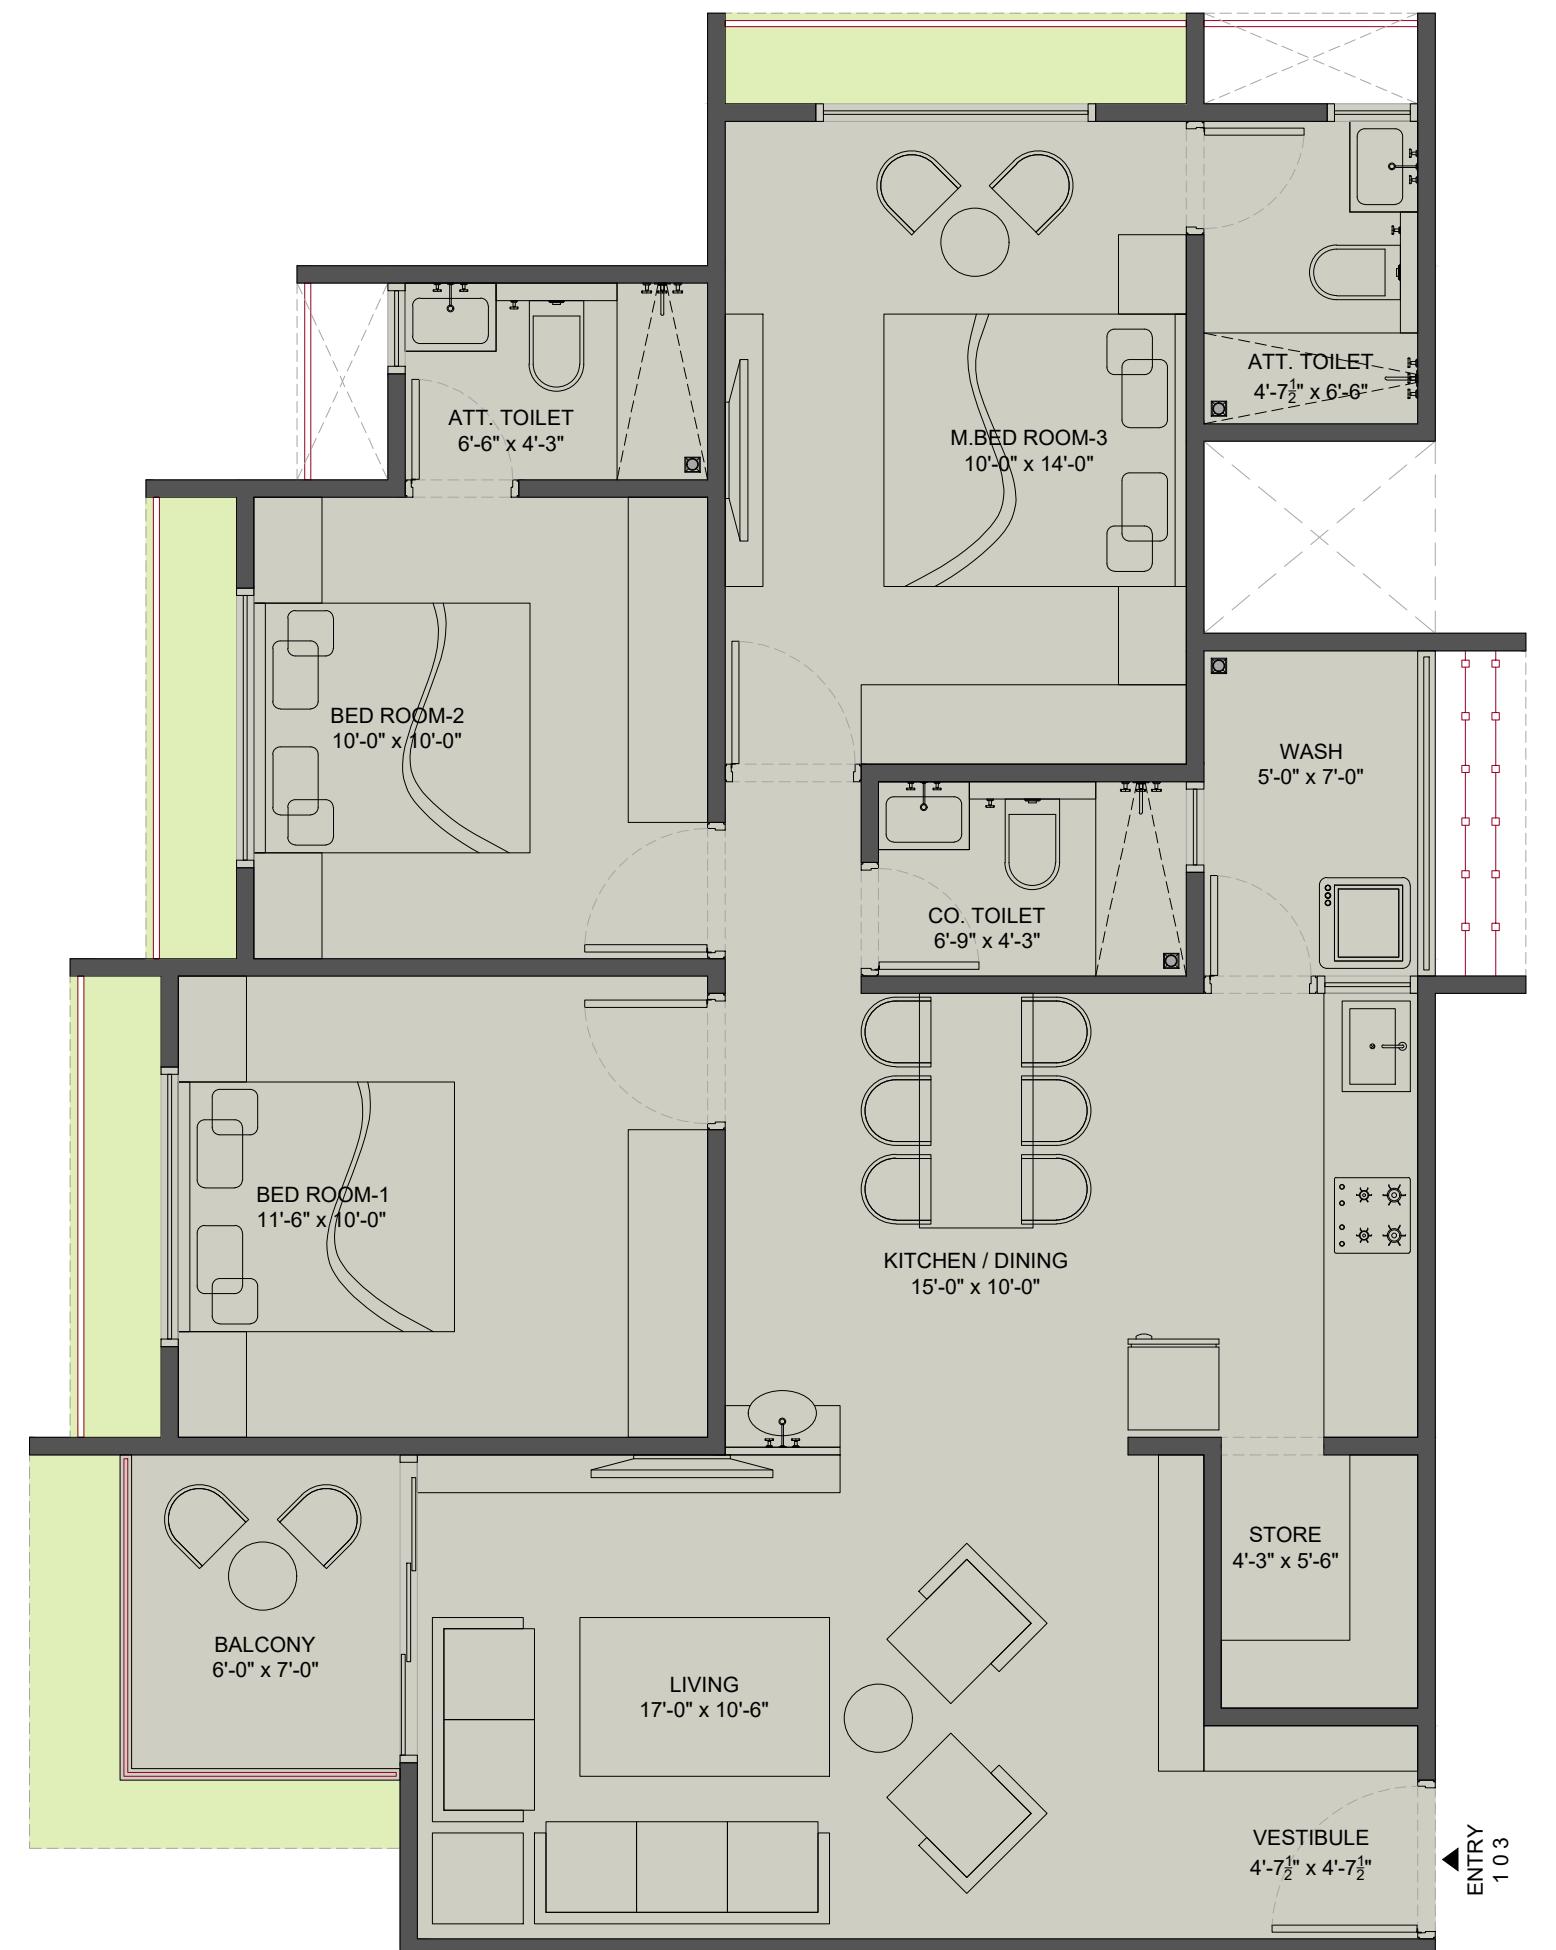

## KEY-PLAN



## REVISION

## DRAWING NAME

**PRESENTATION  
TYPE-C\_UNIT PLAN**

DRAWN BY	RV
DATE	19.11.2024
NOT TO SCALE	

A	0	2	C
---	---	---	---

**T.P. 409 B\_F.P. 229**

AT ZUNDAL, AHMEDABAD.


ISSUE FOR  
DISCUSSION / CONSTRUCTION  
DATE : 00 / 00 / 2024

## A&M DESIGN STUDIO

409, NORTH PLAZA,  
OPP. GOVT. ENGINEERING COLLEGE,  
VISAT - GANDHINAGAR HIGHWAY,  
CHANDIKHEDA, AHMEDABAD - 380005  
T :- +91 9375 47 15 42  
E :- info@aandmstudio.com

## GENERAL NOTES

- ALL DIMENSION ARE IN MILLIMETERS.
- THIS DRAWING IS THE PROPERTY OF A & M DESIGN STUDIO, IS NOT TO BE PRODUCED, COPIED HANDED OVER TO THIRD PARTY OR USED FOR ANY OTHER PURPOSE OTHER THEN FOR WHICH IT IS INTENDED.
- ALL DIMENSION SHALL BE VERIFIED ON SITE PRIOR TO START OF WORK, ANY DISCREPANCY SHALL BE BROUGHT TO THE NOTICE OF THE ARCHITECTS.
- THE CONTRACTOR MUST CHECK ALL DIMENSIONS AND DETAILS AND BE RESPONSIBLE FOR THE SAME, ANY DISCREPANCY SHALL BE BROUGHT TO THE NOTICE OF THE ARCHITECTS BEFORE EXECUTION.
- THIS DRAWING IS TO BE READ AND NOT MEASURED.
- THIS DRAWING SHOULD BE READ IN CONJUNCTION WITH RELEVANT WORKING AND DETAILED DRAWINGS.
- ALL MENTIONED HEIGHTS ARE WITH RESPECT TO INTERNAL FINISH FLOOR LEVEL FOR.
- ALL STRUCTURAL DETAILS FOLLOW THE STRUCTURAL DRAWINGS WITH STRUCTURAL NOTIFICATIONS.

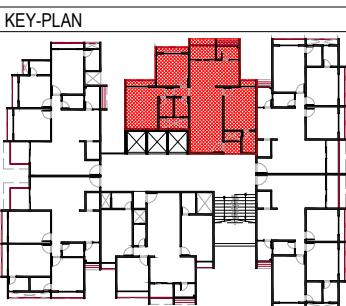

REVISION

DRAWING NAME  
**PRESENTATION**  
TYPE-D\_UNIT PLAN

DRAWN BY	RV
DATE	19.11.2024
NOT TO SCALE	

A 0 2 d

T.P. 409 B\_F.P. 229

AT ZUNDAL, AHMEDABAD.


ISSUE FOR  
DISCUSSION / CONSTRUCTION  
DATE : 00 / 00 / 2024

**A&M DESIGN STUDIO**


409, NORTH PLAZA,  
OPP. GOVT. ENGINEERING COLLEGE,  
VISAT - GANDHINAGAR HIGHWAY,  
CHANDIKHEDA, AHMEDABAD - 380005  
T :- +91 9375 47 15 42  
E :- info@aandmstudio.com

## GENERAL NOTES

- ALL DIMENSION ARE IN MILLIMETERS.
- THIS DRAWING IS THE PROPERTY OF A & M DESIGN STUDIO, IS NOT TO BE PRODUCED, COPIED HANDED OVER TO THIRD PARTY OR USED FOR ANY OTHER PURPOSE OTHER THEN FOR WHICH IT IS INTENDED.
- ALL DIMENSION SHALL BE VERIFIED ON SITE PRIOR TO START OF WORK, ANY DISCREPANCY SHALL BE BROUGHT TO THE NOTICE OF THE ARCHITECTS.
- THE CONTRACTOR MUST CHECK ALL DIMENSIONS AND DETAILS AND BE RESPONSIBLE FOR THE SAME, ANY DISCREPANCY SHALL BE BROUGHT TO THE NOTICE OF THE ARCHITECTS BEFORE EXECUTION.
- THIS DRAWING IS TO BE READ AND NOT MEASURED.
- THIS DRAWING SHOULD BE READ IN CONJUNCTION WITH RELEVANT WORKING AND DETAILED DRAWINGS.
- ALL MENTIONED HEIGHTS ARE WITH RESPECT TO INTERNAL FINISH FLOOR LEVEL FOR.
- ALL STRUCTURAL DETAILS FOLLOW THE STRUCTURAL DRAWINGS WITH STRUCTURAL NOTIFICATIONS.

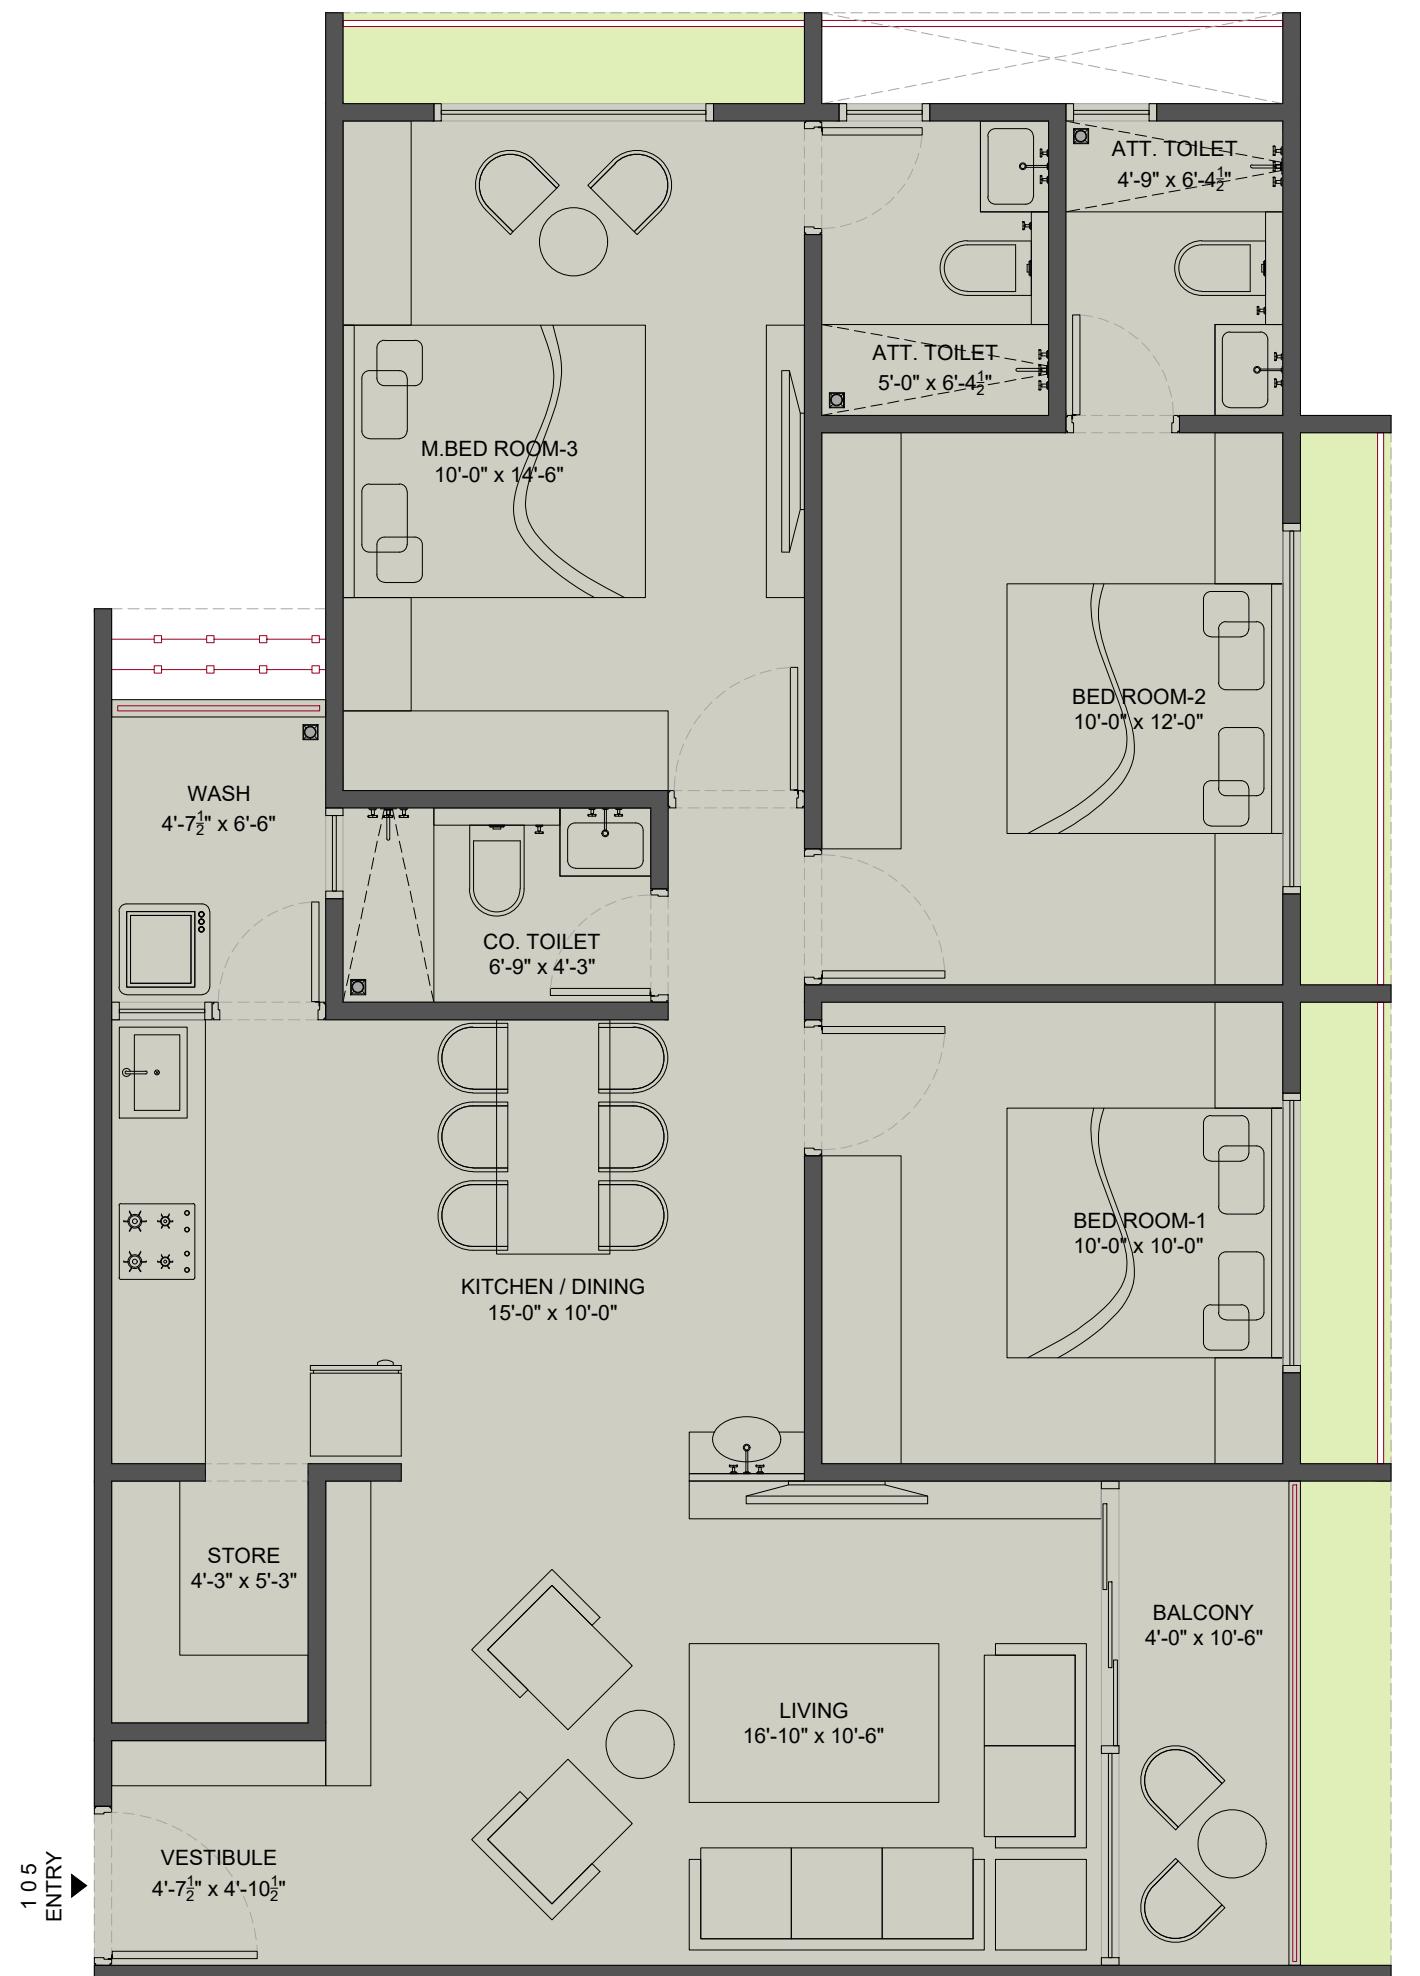

## KEY-PLAN

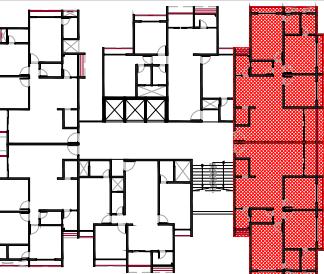

## REVISION

## DRAWING NAME

**PRESENTATION  
TYPE-E\_UNIT PLAN**

DRAWN BY	RV
DATE	19.11.2024
NOT TO SCALE	<input checked="" type="checkbox"/>

**A 0 2 e**

**T.P. 409 B\_F.P. 229**

AT ZUNDAL, AHMEDABAD.

ISSUE FOR  
DISCUSSION / CONSTRUCTION  
DATE : 00 / 00 / 2024

**A&M DESIGN STUDIO**

409, NORTH PLAZA,

OPP. GOVT. ENGINEERING COLLEGE,

VISAT - GANDHINAGAR HIGHWAY,

CHANDIKHEDA, AHMEDABAD - 380005

T :- +91 9375 47 15 42

E :- info@aandmstudio.com